


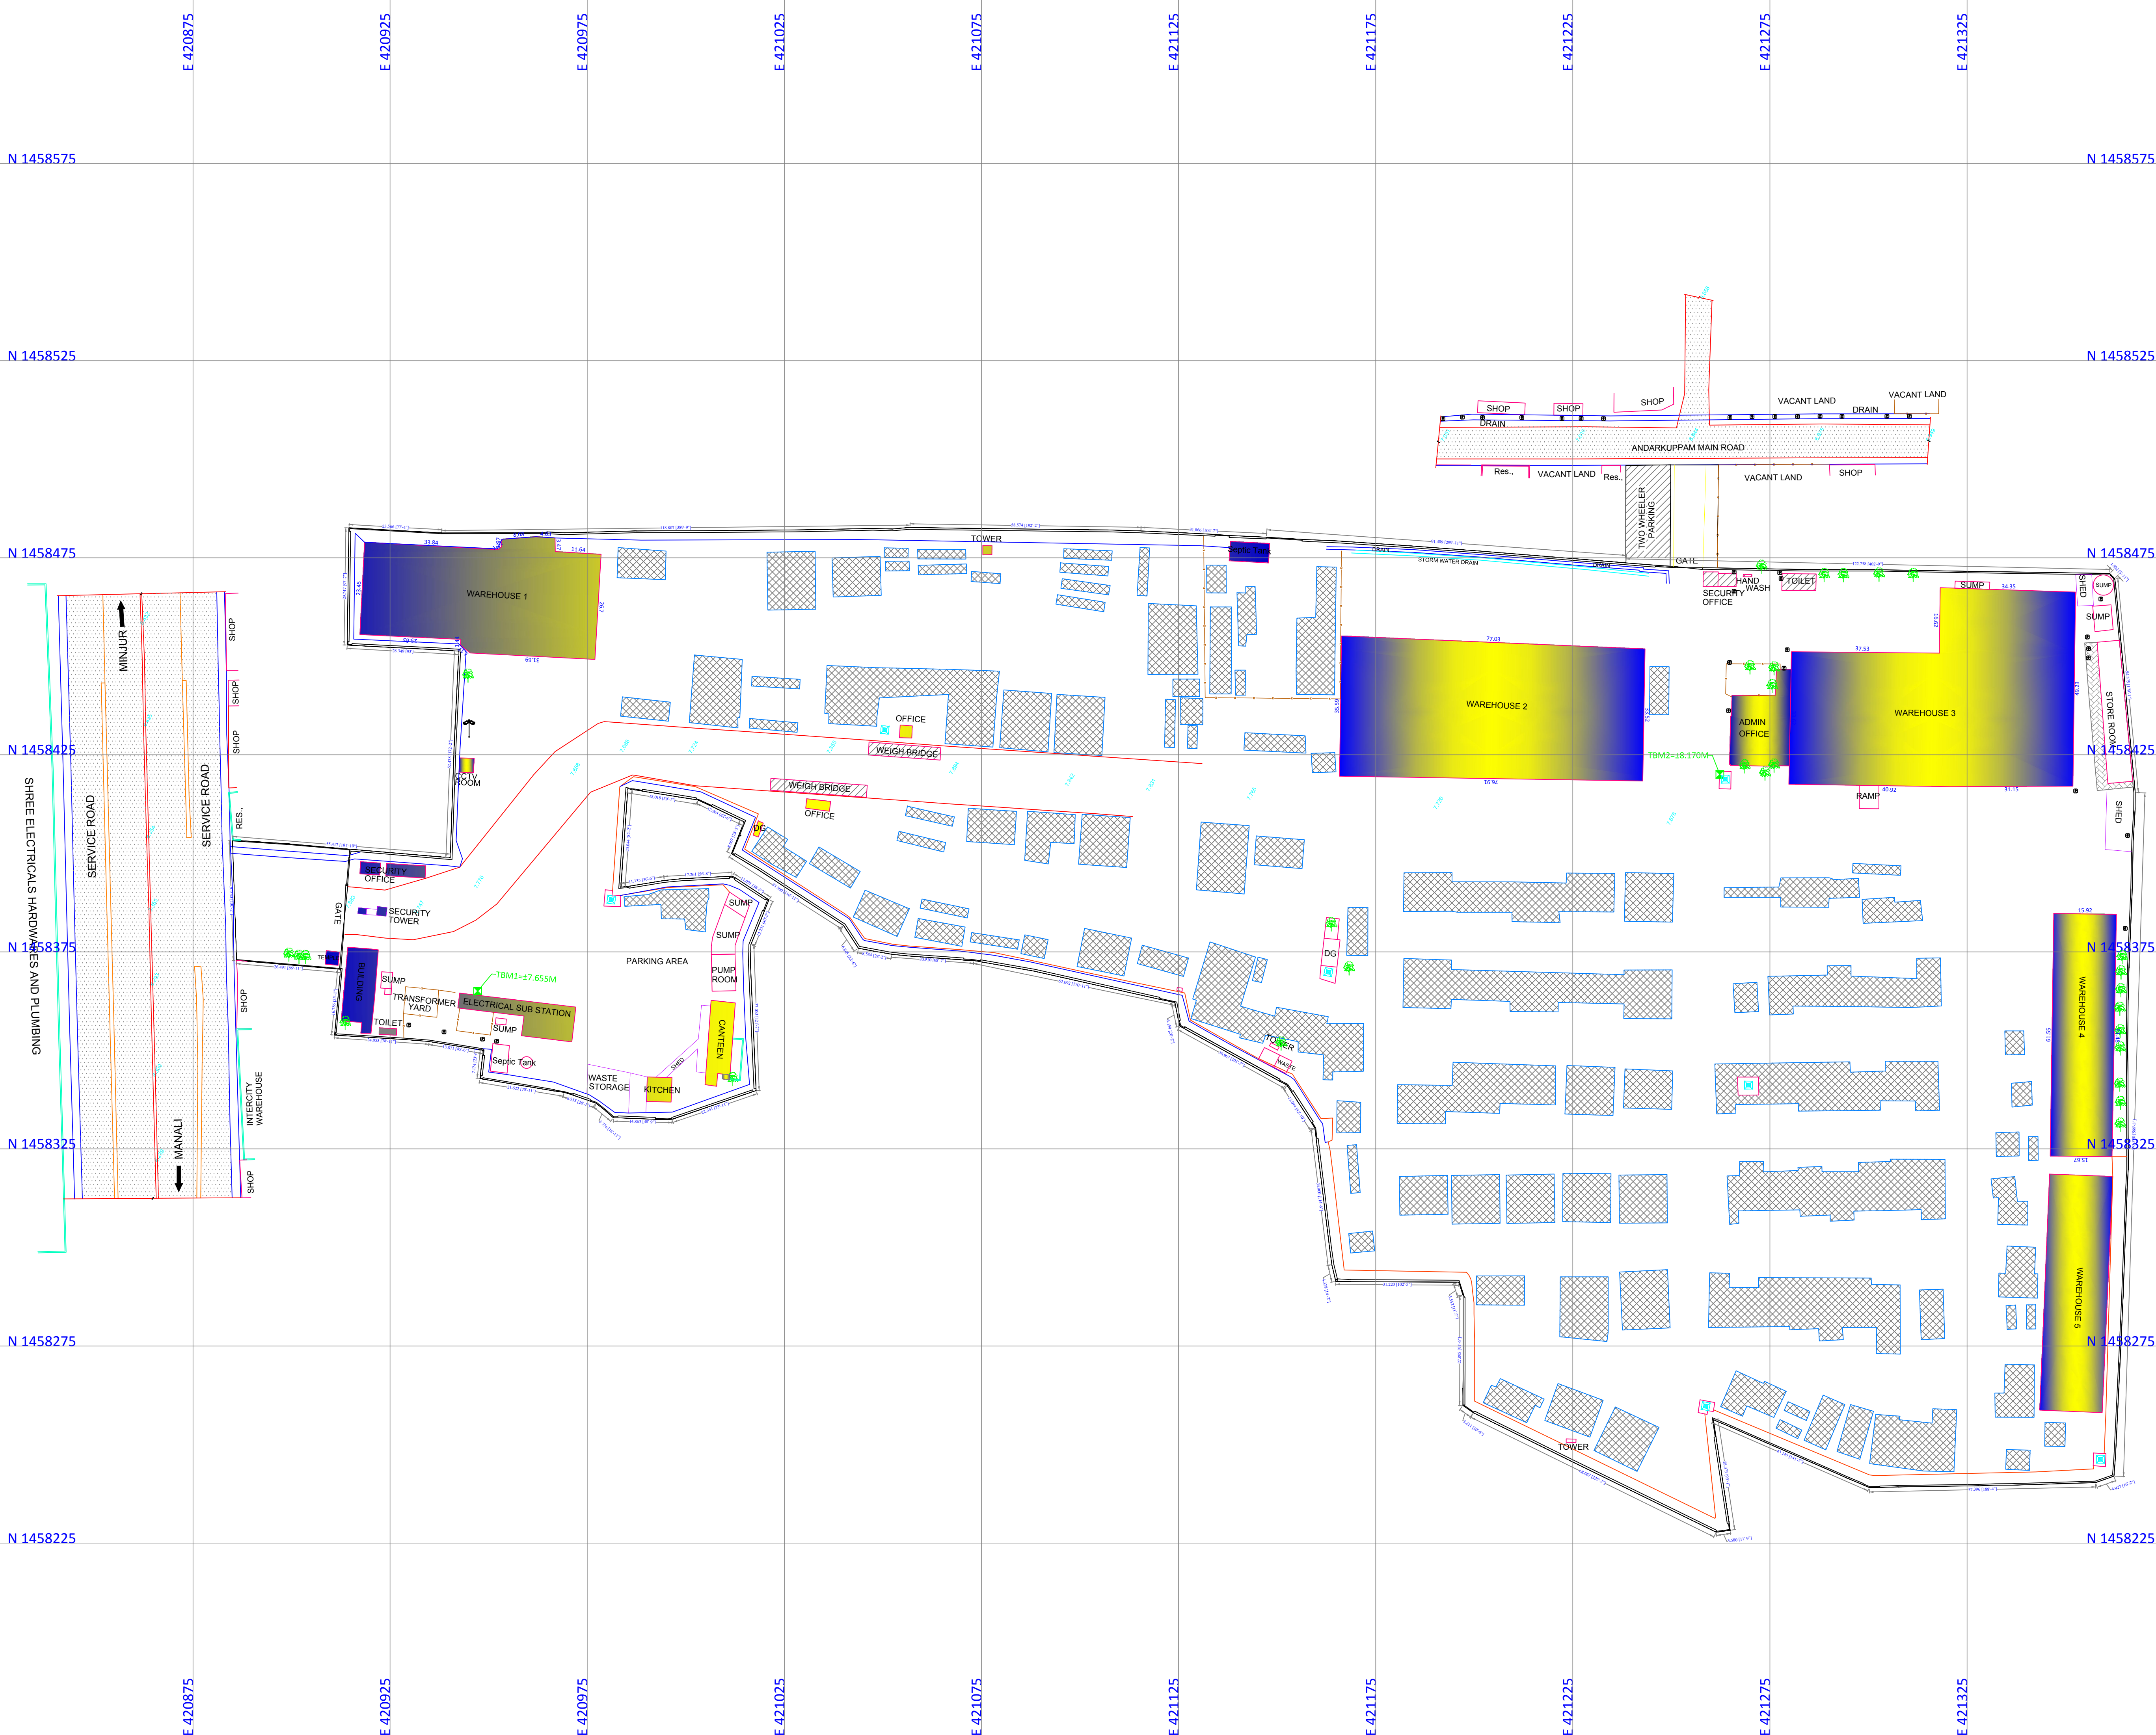

North

W

E

S

D:\RF\2024\APR

A2

RF/051/2024

REV

R1

1. All dimensions are in metres.

2. Surveyed On 29.04.24

3. TBM=10.000 Marked On Electrical sub station

4. Spot Level Interval taken by as per site condation

5. Contour Interval 0.25m.

LEGEND:-

SYMBOL	DESCRIPTION
	SITE BOUNDARY LINE
	COMPOUND WALL
	BUILDING
	LAMP POST
	LEVEL
	CONTOUR LINE WITH VALUE
	CONTAINER
	PAVER BLOCK
	GATE
	ELECTRICAL JUNCTION BOX
	LANE/JUNGLE
	OTHER TREE
	FENCE
	MAN HOLE
	CAMERA POLE
	HIGH MAST LIGHT

Area details

S.no	Description	Area in Sq.m	Area in Sq.ft
1	Warehouse 1	1557.236	16762
2	Warehouse 2	2659.115	28622
3	Warehouse 3	2981.053	32088
4	Warehouse 4	971.746	10460
5	Warehouse 5	956.926	10300
6	Admin Office	293.675	3161
7	Store Room	215.512	2320
8	Canteen	122.273	1316
9	Electrical sub station	178.345	1920
10	Building Near Gate	154.302	1661
11	Security office	76.775	826
12	Kitchen	39.054	420
13	Weigh Bridge	24.735	266
14	Toilet	43.87	472
15	Two Wheeler Parking	285.232	3070
	Total	10559.849	113665

SITE AREA DETAILS

DESCRIPTION	SQ.MT	SQ.FT	ACRES
TOTAL SITE AREA	75783.809	815730	18.726

REVISION

REV.	DATE	SURVEYED	DRAWN	CHD	APPR
C					
B					
A					
0					

SCALE

5.0

2.5

0

5

10

15

20

25

30

35

SCALE: 1:750 (1CM = 7.5M)

PROJECT

Topographical Survey
For GATEWAY
DISTRI PARKS
SOUTH PVT LTD.,
Ponneri High Road,
Manali New Town,
Chennai-600103.

TITLE

Topographical survey

SURVEYED BY:

ROCKFORT ENGINEERING

CIVIL ENGINEERING SURVEY

No:17, 2nd street, Parameshwari
Nagar, Nanddivaram
Guduvanchery, Chennai: 603202.

Tel : 044-47455939

GSM: 9840275939

Web : www.rockfortengineering.in